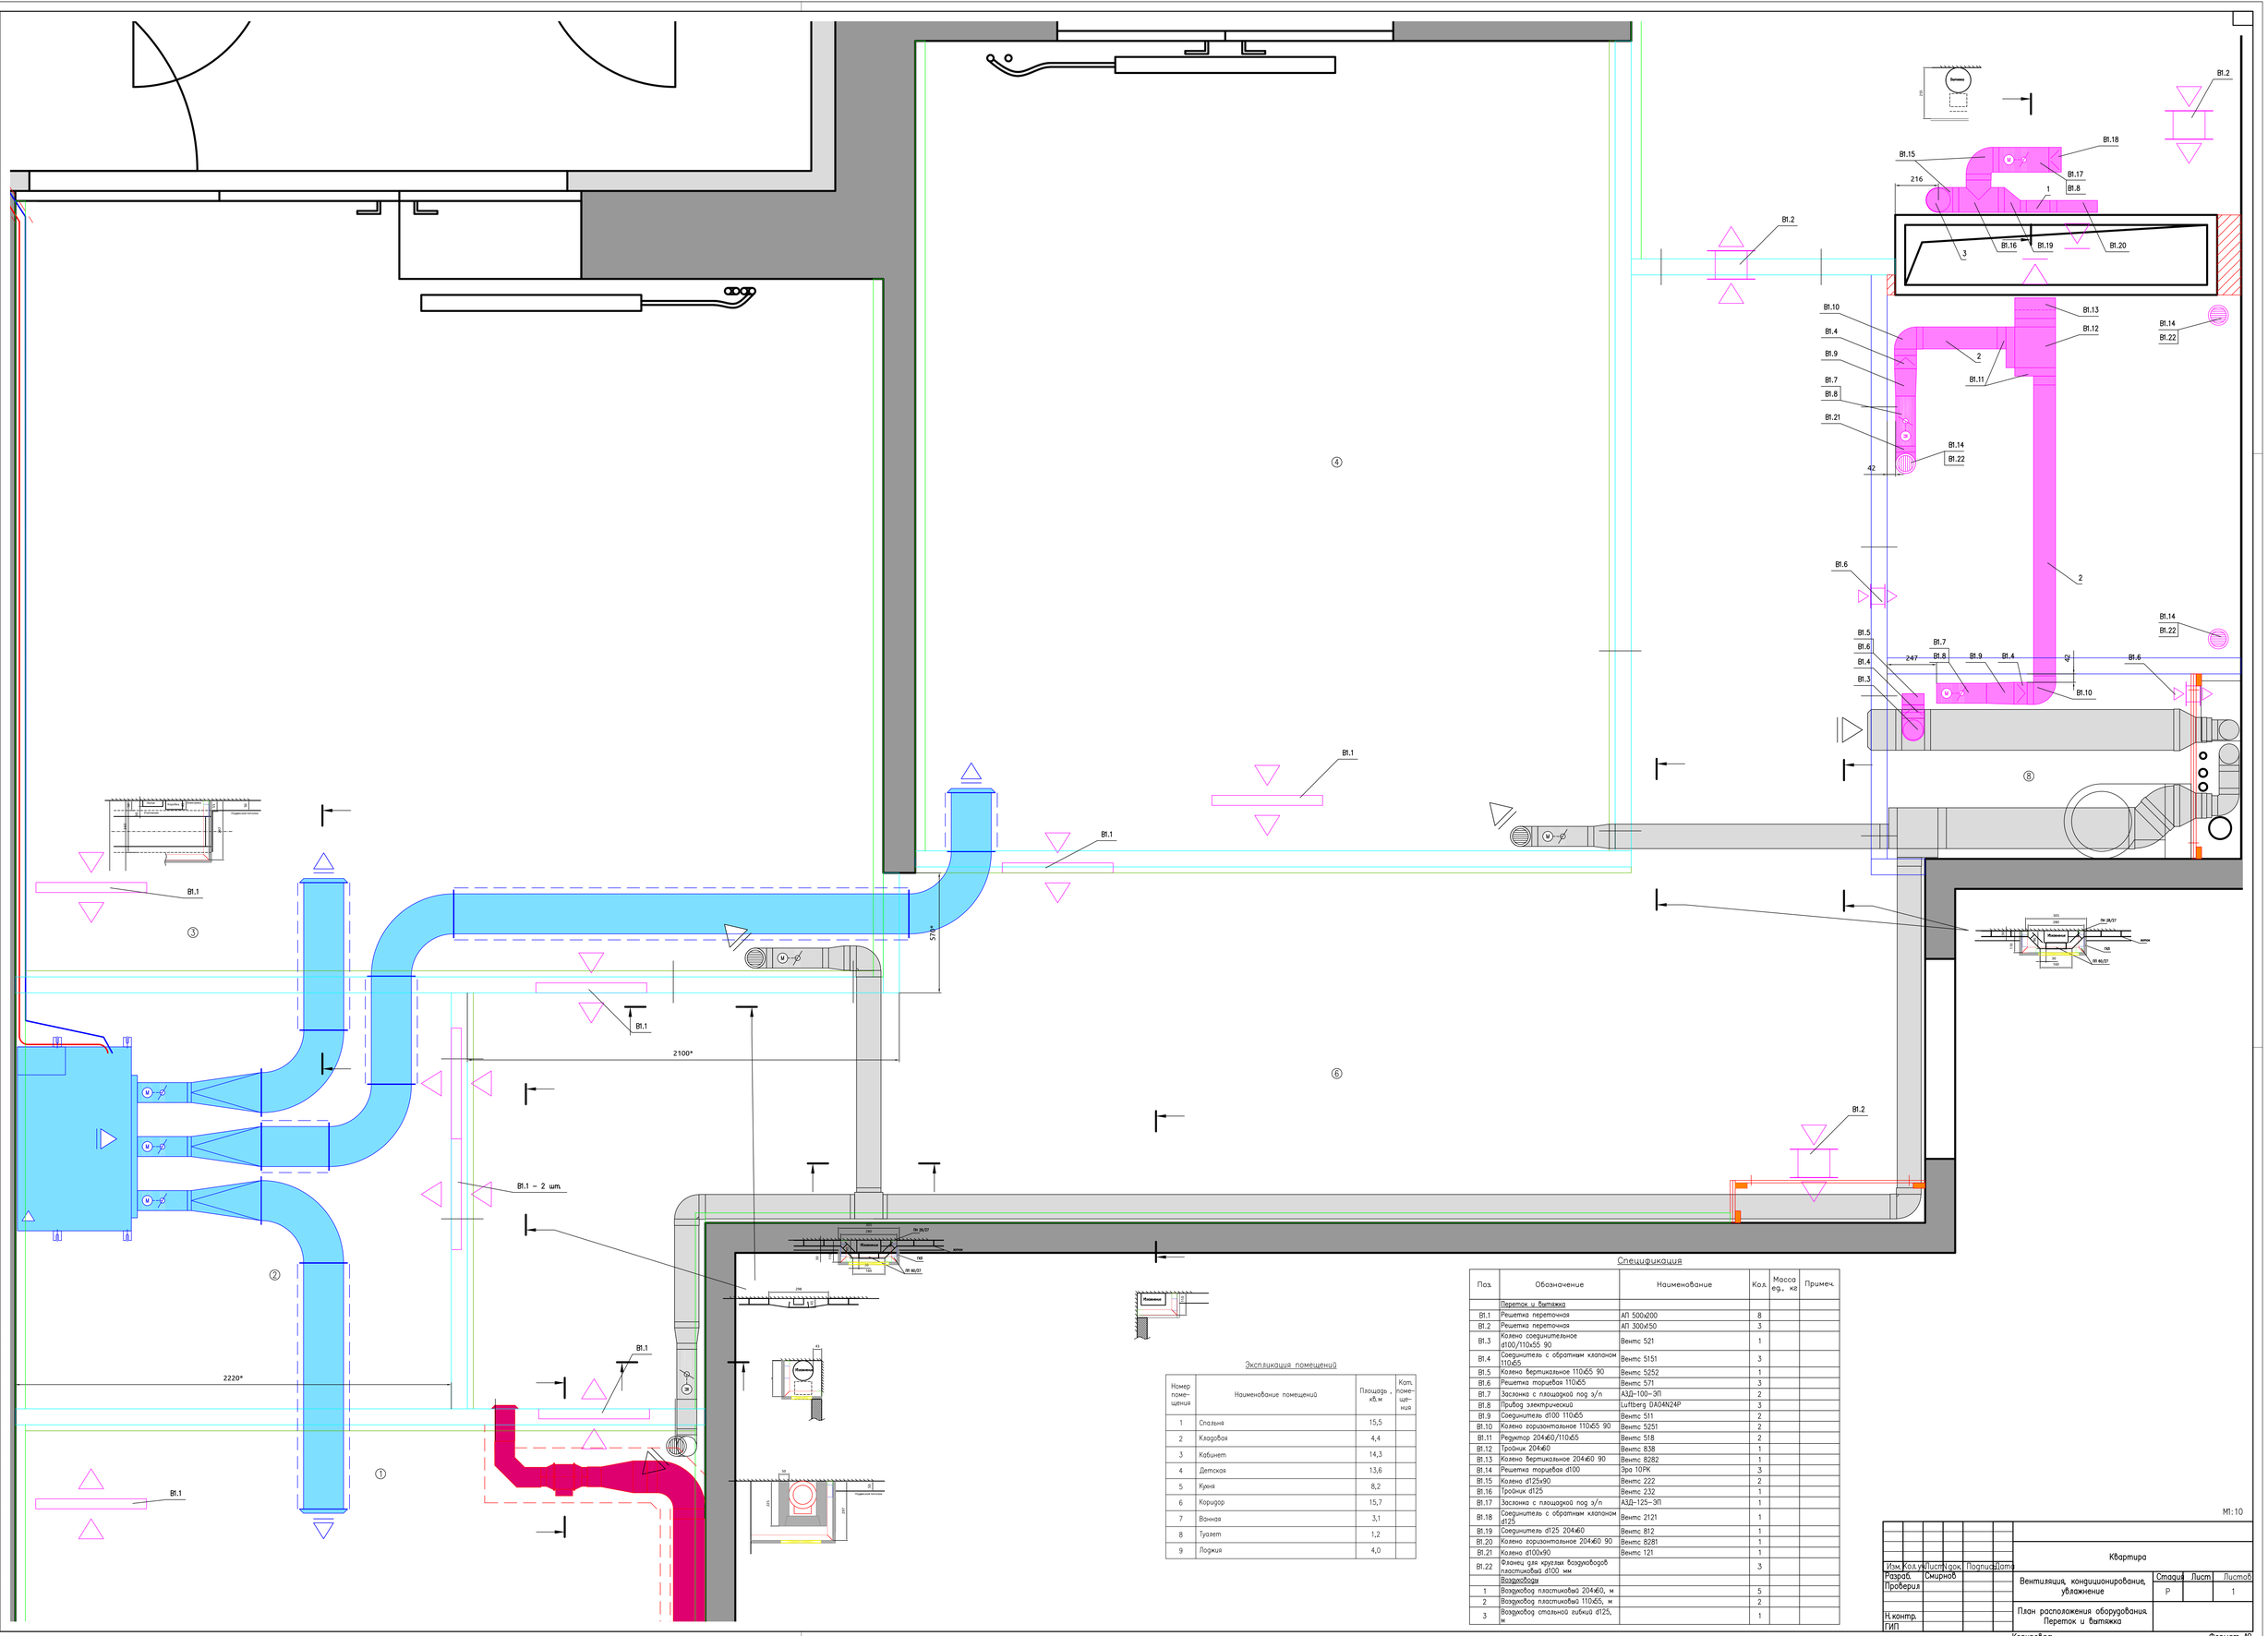

Экспликация помещений

Номер помещения	Наименование помещений	Площадь, кв.м	Кат. помещения
1	Спальня	15,5	
2	Кладовая	4,4	
3	Кабинет	14,3	
4	Детская	13,6	
5	Кухня	8,2	
6	Коридор	15,7	
7	Ванная	3,1	
8	Туалет	1,2	
9	Лоджия	4,0	

Спецификация

Поз.	Обозначение	Наименование	Кол.	Масса ед., кг	Примеч.
	Перетоки и вытяжка				
Вт.1	Решетка переточная	АП 500х200	8		
Вт.2	Решетка переточная	АП 300х150	3		
Вт.3	Колено соединительное d100/110х55 90	Вентс 521	1		
Вт.4	Соединитель с обратным клапаном 110х55	Вентс 5151	3		
Вт.5	Колено вертикальное 110х55 90	Вентс 5252	1		
Вт.6	Решетка торцевая 110х55	Вентс 571	3		
Вт.7	Заслонка с площадкой под э/п	АЗД-100-ЗП	2		
Вт.8	Привод электрический	Luftberg DA04N24P	3		
Вт.9	Соединитель d100 110х55	Вентс 511	2		
Вт.10	Колено горизонтальное 110х55 90	Вентс 5251	2		
Вт.11	Редуктор 204х60/110х55	Вентс 518	2		
Вт.12	Тройник 204х60	Вентс 838	1		
Вт.13	Колено вертикальное 204х60 90	Вентс 8282	1		
Вт.14	Решетка торцевая d100	Эра 10РК	3		
Вт.15	Колено d125х90	Вентс 222	2		
Вт.16	Тройник d125	Вентс 232	1		
Вт.17	Заслонка с площадкой под э/п	АЗД-125-ЗП	1		
Вт.18	Соединитель с обратным клапаном d125	Вентс 2121	1		
Вт.19	Соединитель d125 204х60	Вентс 812	1		
Вт.20	Колено горизонтальное 204х60 90	Вентс 8281	1		
Вт.21	Колено d100х90	Вентс 121	1		
Вт.22	Фланцы для круглых воздуховодов пластиковый d100 мм		3		
	Воздуховоды				
1	Воздуховод пластиковый 204х60, м		5		
2	Воздуховод пластиковый 110х55, м		2		
3	Воздуховод стальной гибкий d125, м		1		