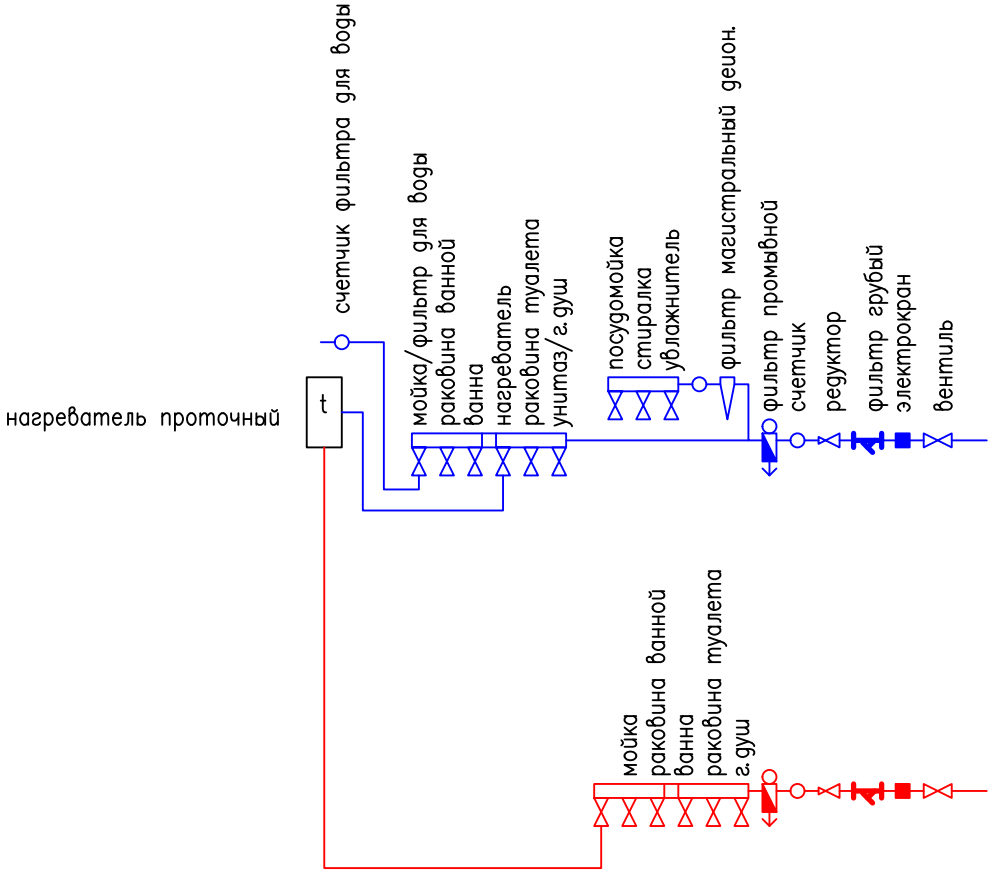

Изм.	Кол. уч.	Лист	N док.	Подпись	Дата	Квартира		
Разраб.		Смирнов				Водоснабжение и канализация	Стадия	Лист	Листов
Проверил							Р		1
Н. контр.						Схема водораспределительного узла			
ГИП									

Согласовано

Взам. инв. #

Подп. и дата

Инв. # подл.

Копировал:

Формат А4