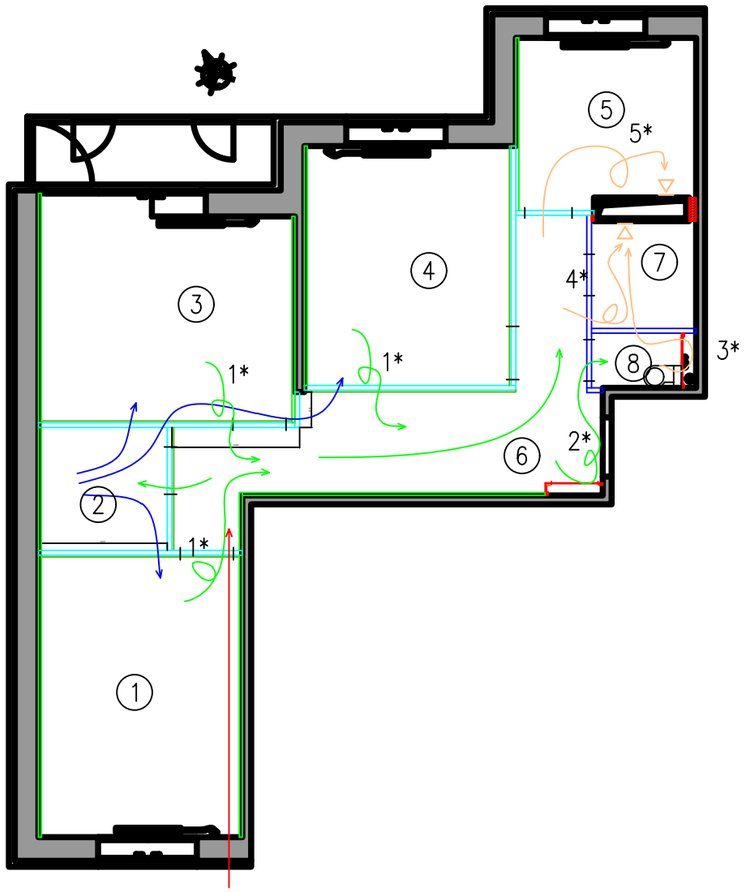

Номер поме-щения	Наименование помещений	Площадь , кв.м	Кат. поме-ще-ния
1	Спальня	15,5	
2	Кладовая	4,4	
3	Кабинет	14,3	
4	Детская	13,6	
5	Кухня	8,2	
6	Коридор	15,7	
7	Ванная	3,1	
8	Туалет	1,2	
9	Лоджия	4,0	

Примеч.

1. Движение воздуха в комнатах: основной объем комнаты – запотолочное пространство комнаты – основной объем коридора.
2. Движение воздуха в техзоне: основной объем коридора – техзона – запотолочное пространство коридора – запотолочное пространство туалета.
3. Движение воздуха в туалете: запотолочное пространство коридора – основной объем туалета – стояки – запотолочное пространство туалета – вытяжка в ванной.
4. Движение воздуха в ванной: запотолочное пространство коридора – запотолочное пространство ванной – основной объем ванной – вытяжка в ванной.
5. Движение воздуха на кухне: основной объем – запотолочное пространство – вытяжка.

Условные обозначения.

- Приток
- Кондиционирование
- Переток (промежуточные зоны)
- Вытяжка

М1:100

Изм.	Кол. уч.	Лист	N док.	Подпись	Дата	Квартира			
Разраб.		Смирнов				Вентиляция, кондиционирование, увлажнение	Стадия	Лист	Листов
Проверил							Р		
Н. контр.						План воздухообмена			
ГИП									

Согласовано

Взам. инв. #

Подп. и дата

Инв. # подл.

Копировал:

Формат А3